


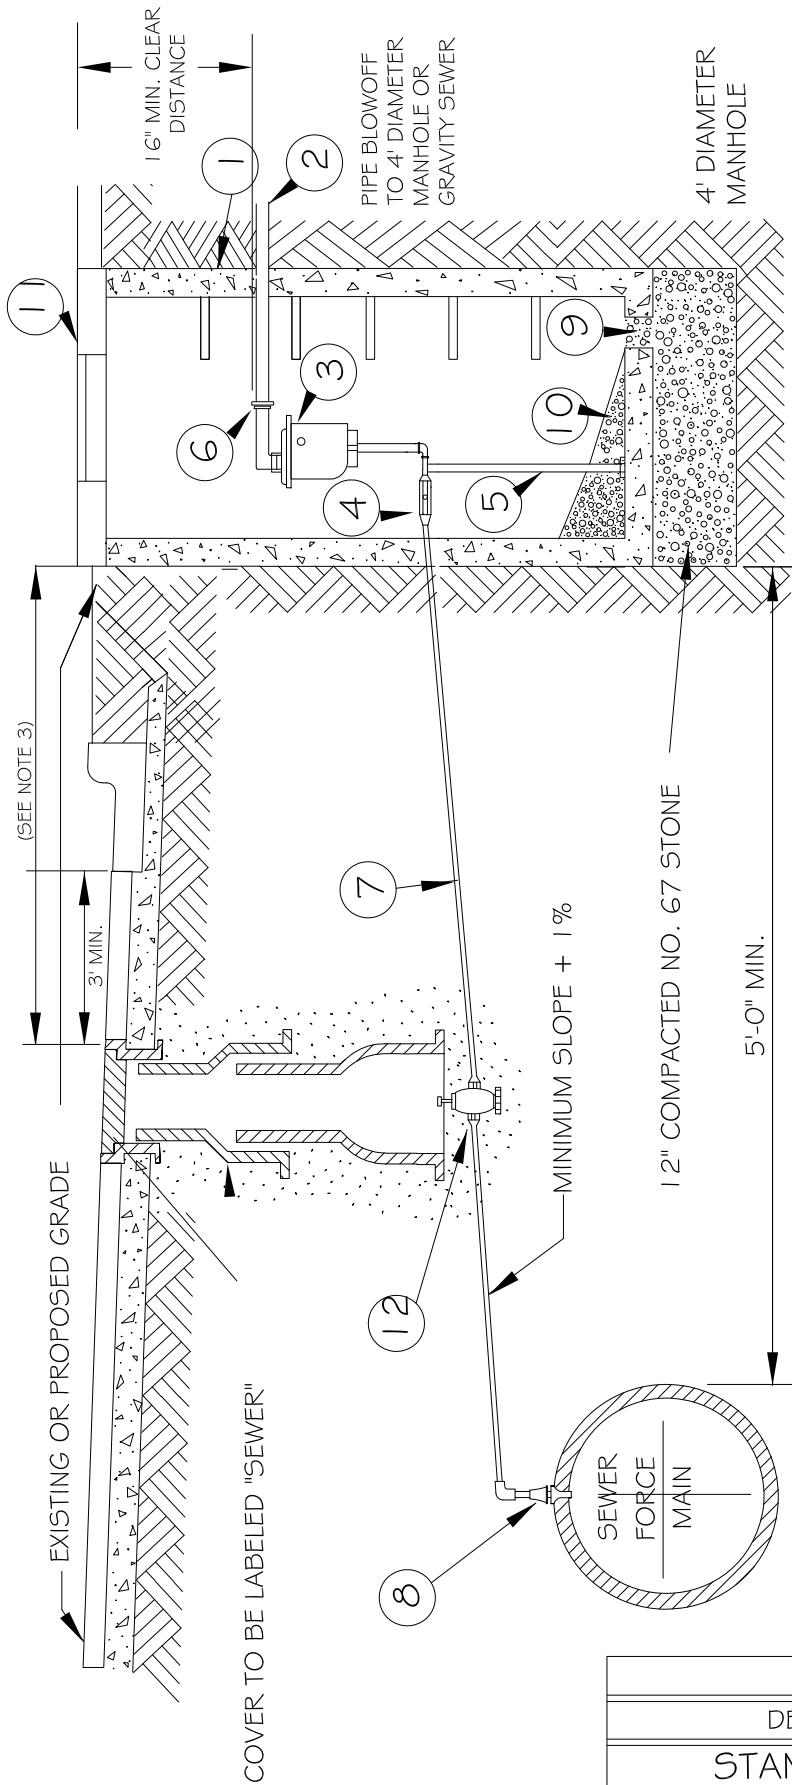

BILL OF MATERIALS

1	PRECAST MANHOLE W/ FLAT TOP
2	BLOW OFF PIPE SCD 80 PVC
3	2" AIR RELEASE VALVE
4	2"-SS BALL VALVE
5	PIPE STAND SUPPORT SS
6	2" UNION SCD 80 PVC
7	2" TYPE "K", SOFT COPPER WITH FLARED ELBOW
8	CORPORATION COCK
9	6" DIAMETER DRAIN
10	GROUT, 1/8" TO 1'-0" MIN. SLOPE TO DRAIN
11	36" x 30" HALLIDAY HATCH, ALUM.
12	2"-GATE VALVE

NOTE:

1. AIR RELEASE/VACUUM VALVE TO BE A.R.I. FLOW CONTROL MODEL SAAR SHORT VERSION D-025 SS (STAINLESS STEEL)
2. THE AIR RELEASE MANHOLE SHALL BE INSTALLED IN THE SHOULDER OR AS DIRECTED BY THE ENGINEER.
3. FOR MAINS LOCATED OUTSIDE OF STREET RIGHT-OF-WAYS THE MAXIMUM DISTANCE BETWEEN THE MANHOLE AND THE VALVE BOX SHOULD BE THREE (3) FEET.
4. MAIN SHALL BE DEEP ENOUGH TO ACCOMMODATE INSTALLATION AS SHOWN

SEE STANDARD DETAIL S-4 & S-5 TO INSURE PROPER BACKFILL.

CITY OF RALEIGH				
DEPARTMENT OF PUBLIC UTILITIES				
STANDARD SEWER FORCE MAIN AIR RELEASE VALVE				
DWG. NO.	REVISIONS	DATE	REVISIONS	DATE
S-9		7-14-82		12-31-91
	LBN	9-30-04	RRH	3-30-00